

LEGEND OF EXISTING FEATURES



- SITE BOUNDARY
- EASEMENT
- EXISTING SPOT ELEVATIONS/CONTOURS
- EXISTING DIRECTION OF DRAINAGE/SWALE
- EXISTING CURB
- EXISTING BUILDING
- EXISTING FENCE
- EXISTING EMBANKMENT (SLOPE AS NOTED)
- EXISTING MAN DOOR

LEGEND OF PROPOSED FEATURES


- PROPOSED SPOT ELEVATIONS
EX = MAINTAIN EXISTING
- DIRECTION OF DRAINAGE
- CONSTRUCTION ACCESS (SEE DETAIL)
- SEDIMENT CONTROL FENCE (SEE DETAIL)
- SILT SACK (SEE DETAIL)
- REMOVALS
- GRAVEL BOUNDARY

CONSTRUCTION NOTES AND SPECIFICATIONS


- GENERAL
 - THIS PLAN NOT FOR CONSTRUCTION UNTIL SIGNED AND SEALED BY ENGINEER AND APPROVED BY CITY OF TORONTO.
 - THIS PLAN IS TO BE USED FOR SERVING AND GRADING ONLY. ANY OTHER INFORMATION SHOWN IS FOR ILLUSTRATION PURPOSES ONLY. THIS PLAN MUST NOT BE USED TO SITE THE PROPOSED BUILDING.
 - NO CHANGES ARE TO BE MADE WITHOUT THE APPROVAL OF THE DESIGN ENGINEER.
 - THIS PLAN IS NOT TO BE REPRODUCED IN WHOLE OR IN PART WITHOUT THE PERMISSION OF MTE CONSULTANTS INC.
 - PRIOR TO CONSTRUCTION, THE CONTRACTOR MUST:
 - CHECK AND VERIFY ALL EXISTING CONDITIONS, LOCATIONS AND ELEVATIONS WHICH INCLUDES BUT IS NOT LIMITED TO THE BENCHMARK ELEVATIONS, EXISTING SERVICE CONNECTIONS AND EXISTING INVERTS. REPORT ALL DISCREPANCIES TO THE ENGINEER PRIOR TO PROCEEDING.
 - OBTAIN ALL UTILITY LOCATES AND REQUIRE PERMITS AND LICENSES.
 - CONFIRM ALL DRAWINGS USED FOR CONSTRUCTION ARE OF THE MOST RECENT REVISION.
 - THE CONTRACTOR SHALL ASSUME ALL LIABILITY FOR ANY DAMAGE TO EXISTING WORKS. THE CONTRACTOR IS RESPONSIBLE FOR RESTORATION OF ALL DAMAGED AND/OR DISTURBED PROPERTY WITHIN THE MUNICIPAL RIGHT-OF-WAY TO CITY OF TORONTO STANDARDS.
 - ALL WORK TO CONFORM TO THE LATEST CITY OF TORONTO STANDARD DRAWINGS AND SPECIFICATIONS AS WELL AS THE LATEST ADOPTED ONTARIO PROVINCIAL STANDARD DRAWINGS AND SPECIFICATIONS.
 - ALL WORK SHALL BE COMPLETED IN ACCORDANCE WITH THE CURRENT OCCUPATIONAL HEALTH AND SAFETY ACT AND REGULATIONS FOR CONSTRUCTION PROJECTS. THE GENERAL CONTRACTOR SHALL BE DEEMED TO BE THE CONSTRUCTOR AS DEFINED IN THE ACT.
 - ALL TEMPORARY TRAFFIC CONTROL AND SIGNAGE DURING CONSTRUCTION SHALL BE IN ACCORDANCE WITH CURRENT ONTARIO TRAFFIC MANUAL BOOK 7: TEMPORARY CONDITIONS FIELD EDITION.
 - THE CONTRACTOR SHALL RECTIFY ALL DISTURBED AREAS TO THE ORIGINAL CONDITION OR BETTER AND TO THE SATISFACTION OF THE EXECUTIVE DIRECTOR, TECHNICAL SERVICES.
 - PRIOR TO COMMENCING ANY WORK WITHIN THE MUNICIPAL RIGHT OF WAY, THE CONTRACTOR OR DEVELOPER OR CONSULTANT WILL OBTAIN ALL NECESSARY ROAD OCCUPANCY PERMITS FROM THE CITY'S RIGHT-OF-WAY MANAGEMENT DIVISION.
 - CONTRACTOR IS RESPONSIBLE FOR CONTACTING ENGINEER 48 HRS PRIOR TO COMMENCING WORK TO ARRANGE FOR INSPECTION. ENGINEER TO DETERMINE DEGREE OF INSPECTION AND TESTING REQUIRED FOR CERTIFICATION OF UNDERGROUND SERVICE INSTALLATION AS MANDATED BY ONTARIO BUILDING CODE, DIVISION C, PART 1, SECTION 1.2.2. GENERAL REVIEW FAILURE TO NOTIFY ENGINEER WILL RESULT IN EXTENSIVE POST CONSTRUCTION INSPECTION AT CONTRACTORS EXPENSE.
 - CONTRACTOR TO OBTAIN WRITTEN PERMISSION FROM ADJACENT PROPERTY OWNER PRIOR TO ENTERING UPON NEIGHBOURING LANDS TO UNDERTAKE ANY WORK. COPIES OF THESE LETTERS OF CONSENT SHALL BE SUBMITTED TO THE DEPARTMENT OF PUBLIC WORKS FOR APPROVAL PRIOR TO ANY WORK BEING PERFORMED. FAILURE TO COMPLY WITH THE ABOVE IS CONTRACTOR'S OWN RISK.
 - FILTER FABRIC TO BE TERRAFIX 200K OR APPROVED EQUIVALENT.
 - MAXIMUM GRADED SLOPE TO BE 3:1. SLOPES GREATER THAN 3:1 TO BE LANDSCAPED AREA WITH LOW MAINTENANCE GROUND COVER.
 - THE CONTRACTOR SHALL BE RESPONSIBLE FOR ALL TRAFFIC AND SAFETY MEASURES DURING THE CONSTRUCTION PERIOD INCLUDING TRAFFIC CONTROL, TRAFFIC SIGNALS, TRAFFIC LIGHTS, ALL NECESSARY SIGNALS, DELINEATORS, MARKERS, AND BARRIERS. ALL TEMPORARY TRAFFIC CONTROL AND SIGNAGE DURING CONSTRUCTION SHALL BE IN ACCORDANCE WITH CURRENT ONTARIO TRAFFIC MANUAL BOOK 7: TEMPORARY CONDITIONS FIELD EDITION.
 - THE POSITION OF POLE LINES, CONDUITS, WATERMANS, SEWERS AND OTHER UNDERGROUND AND OVERGROUND UTILITIES AND STRUCTURES IS NOT NECESSARILY SHOWN ON THE CONTRACT DRAWINGS, AND WHERE SHOWN, THE ACCURACY OF THE POSITION OF SUCH UTILITIES AND STRUCTURES IS NOT GUARANTEED. BEFORE STARTING WORK, THE CONTRACTOR SHALL INFORM HIMSELF OF THE EXACT LOCATION OF ALL SUCH UTILITIES AND STRUCTURES AND SHALL ASSUME ALL LIABILITY FOR DAMAGE TO THEM.
 - CONTRACTOR TO MAINTAIN A "CONFINED TRENCH CONDITION" IN ALL SEWER AND SERVICE TRENCHES.
 - THE CONTRACTOR SHALL RECTIFY ALL DISTURBED AREAS TO THE ORIGINAL CONDITIONS OR BETTER AND TO THE SATISFACTION OF THE CONTRACT ADMINISTRATOR.
 - FOLLOWING COMPLETION OF PROPOSED WORKS AND PRIOR TO OCCUPANCY INSPECTION, ALL STORM AND SANITARY SEWERS ARE TO BE FLUSHED, AND ALL CATCHBASIN AND CATCH-BASIN MANHOLE SUMPS ARE TO BE CLEANED OF DEBRIS AND SILT.
 - PRIOR TO THE INSTALLATION OF ANY GRANULAR MATERIAL, THE SOIL CONSULTANT MUST HAVE ISSUED A COMPACTION CERTIFICATE FOR APPROVAL.
- EROSION AND SEDIMENT CONTROL
 - CONTRACTOR TO INSTALL EROSION CONTROL MEASURES AS SHOWN PRIOR TO CONSTRUCTION AND MAINTAIN IN GOOD CONDITION UNTIL CONSTRUCTION IS COMPLETED AND VEGETATIVE COVER IS ESTABLISHED.
 - ALL SILT FENCING TO BE INSTALLED PRIOR TO ANY AREA GRADING, EXCAVATING OR DEMOLITION COMMENCING.
 - EROSION CONTROL FENCING TO BE INSTALLED AROUND BASE OF ALL STOCKPILES.
 - EROSION PROTECTION TO BE PROVIDED AROUND ALL STORM AND SANITARY PITS AND CDS.
 - ADDITIONAL EROSION CONTROL MEASURES MAY BE REQUIRED AS SITE DEVELOPMENT PROGRESSES. CONTRACTOR TO PROVIDE ALL ADDITIONAL EROSION CONTROL STRUCTURES.
 - EROSION CONTROL STRUCTURES TO REMAIN IN PLACE UNTIL ALL DISTURBED GROUND SURFACES HAVE BEEN REESTABLISHED.
 - NO ALTERNATE METHODS OF EROSION PROTECTION SHALL BE PERMITTED UNLESS APPROVED BY THE ENGINEER AND THE DEPARTMENT OF PUBLIC WORKS.
 - CONTRACTOR TO CLEAN ROADWAY AND SIDEWALKS OF SEDIMENTS RESULTING FROM CONSTRUCTION TRAFFIC FROM THE SITE EACH DAY.
 - CONTRACTOR MUST REMOVE EROSION AND SEDIMENTATION FENCING PRIOR TO COMPLETION OF PROJECT. CONTRACTOR TO HAVE EROSION AND SEDIMENTATION FENCE INSPECTED WHEN VEGETATION HAS ESTABLISHED, BUT PRIOR TO FENCE BECOMING OVERGROWN. ENGINEER'S REPRESENTATIVE TO DETERMINE IF VEGETATION HAS REACHED THE CRITICAL POINT AND WILL THEN INSTRUCT CONTRACTOR TO REMOVE FENCE.
- MAINTENANCE RECOMMENDATIONS
 - REMOVE SEDIMENT AND CONTAMINANTS WEEKLY AND REINSTATE STORM WATER MANAGEMENT FACILITY ACCORDING TO THE DESIGN OUTLINED ON THIS PLAN.
 - EROSION CONTROL STRUCTURES TO BE MONITORED REGULARLY AND ANY DAMAGE REPAIRED IMMEDIATELY. SEDIMENTS TO BE REMOVED WHEN ACCUMULATIONS REACH A MAXIMUM OF 1/3 THE HEIGHT OF THE FENCE.
 - OWNER'S REPRESENTATIVE TO MONITOR EROSION CONTROL STRUCTURES TO ENSURE FENCING IS INSTALLED AND MAINTENANCE IS PERFORMED TO CITY REQUIREMENTS.
 - THE OWNER SHALL ENTER INTO A MAINTENANCE AGREEMENT WITH AN APPROPRIATE CONTRACTOR FOR THE MAINTENANCE OF THE PROPOSED STORM TANK AND PROPOSED OIL GRIT SEPARATOR UNIT AS RECOMMENDED BY THE MANUFACTURER.
- GRADING AND ROAD/PAVEMENT NOTES
 - ALL AREA GRADING AND RESULTING DRAINAGE PATTERNS SHALL NOT ADVERSELY AFFECT ADJACENT LANDS.
 - THE STORM DRAINAGE SHALL BE SELF CONTAINED WITHIN THE SUBJECT PROPERTY UNTIL IT CAN BE DISCHARGED, REUSED, INFILTRATED AND/OR EVAPORATED IN A MANNER ACCEPTABLE TO THE CITY.
 - MINIMUM GENERALLY ACCEPTED GRAIENT - 1.0 PERCENT.
 - MAXIMUM GENERALLY ACCEPTED GRAIENT - 5.0 PERCENT.
 - MAXIMUM ACCEPTABLE SLOPE 3 PARTS HORIZONTAL TO 1 PART VERTICAL.
 - NO ALTERATIONS TO EXISTING BOUNDARY ELEVATIONS OR ADJACENT LANDS SHALL BE UNDERTAKEN UNLESS WRITTEN AGREEMENT WITH THE ADJACENT PROPERTY OWNER IS OBTAINED AND SUBMITTED IN A FORMAT ACCEPTABLE TO THE CITY.
 - MINIMUM SWALE GRAIENT - 2.0 PERCENT (UNLESS OTHERWISE NOTED).
 - MINIMUM SWALE DEPTH - 150mm.
 - ALL SWALES OR DITCHES HAVING A VELOCITY IN EXCESS OF 1.5 METRES/SECOND SHALL BE DESIGNED TO INCORPORATE EROSION PROTECTION.
 - THE MINIMUM GRAIENT ON ANY DRIVEWAY SHALL BE 1.0 PERCENT. THE MAXIMUM DRIVEWAY GRAIENT IS 8.0 PERCENT. DRIVEWAY RAMP GRADES TO UNDERGROUND PARKING STRUCTURE AS SHOWN ON C2.1 DRAWING.
 - MAXIMUM FLOODING DEPTH OF 0.3 METERS.
 - PROPOSED SPOT ELEVATIONS WILL BE SHOWN FOR ASPHALT, LANDSCAPED AREA OR CONCRETE AREAS UNLESS OTHERWISE NOTED. TOP OF CURB ELEVATIONS ARE 0.15 METRE ABOVE ASPHALT ELEVATIONS EXCEPT AT CURB DEPRESSIONS AND WHEEL CHAIR RAMPS.
 - THE CONCRETE CURB, CONCRETE SIDEWALK (IF APPLICABLE) AND ALL RESTORATION ALONG FRONTING ROADWAYS TO THE SITE MUST BE CONSTRUCTED AND CARRIED OUT IN ACCORDANCE WITH ALL APPLICABLE AND CURRENT CITY OF TORONTO STANDARDS, WHICH INCLUDE BUT ARE NOT LIMITED TO:
 - T-26.02-8: ROADWAY SIDEWALK
 - T-31.05-8: DRIVEWAY THICKNESS
 - T-31.05-2: CONCRETE SIDEWALK WITH BOULEVARD
 - T-31.03-10: DEPRESSED CURB AND SIDEWALK RAMP
 - T-35.01-1: URBAN ENTRANCES
 - T-60.01-1: CONC. CURB (BORDERING DRIVEWAY RETURN CURB AT ENTRANCES)
 - T-60.05-1: CONCRETE CURB AND GUTTER.
 - ALL AREA GRADING AND RESULTING DRAINAGE PATTERNS SHALL NOT ADVERSELY AFFECT ADJACENT LANDS.

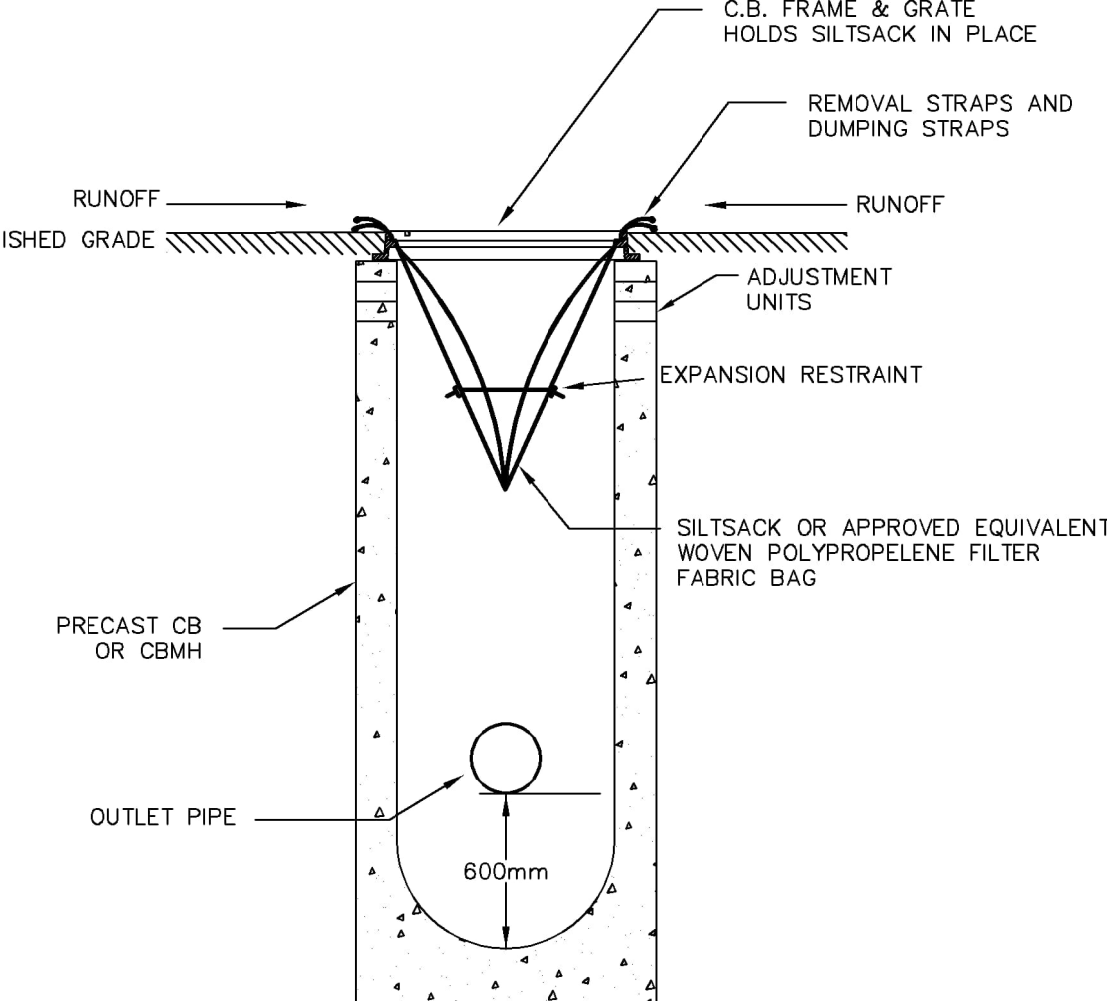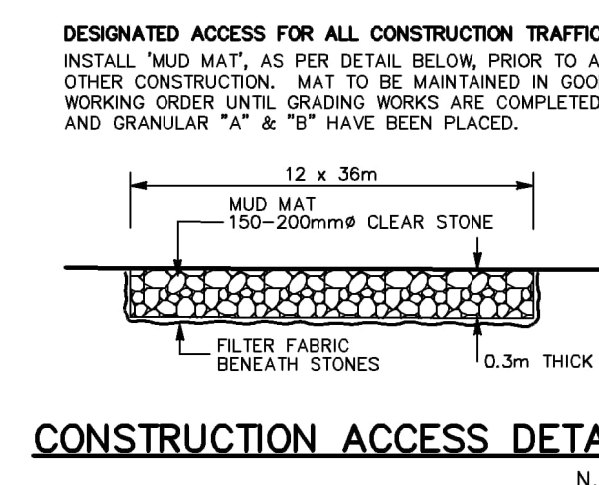


TEMPORARY SILTSACK SILTATION CONTROL IN CB N.T.S.

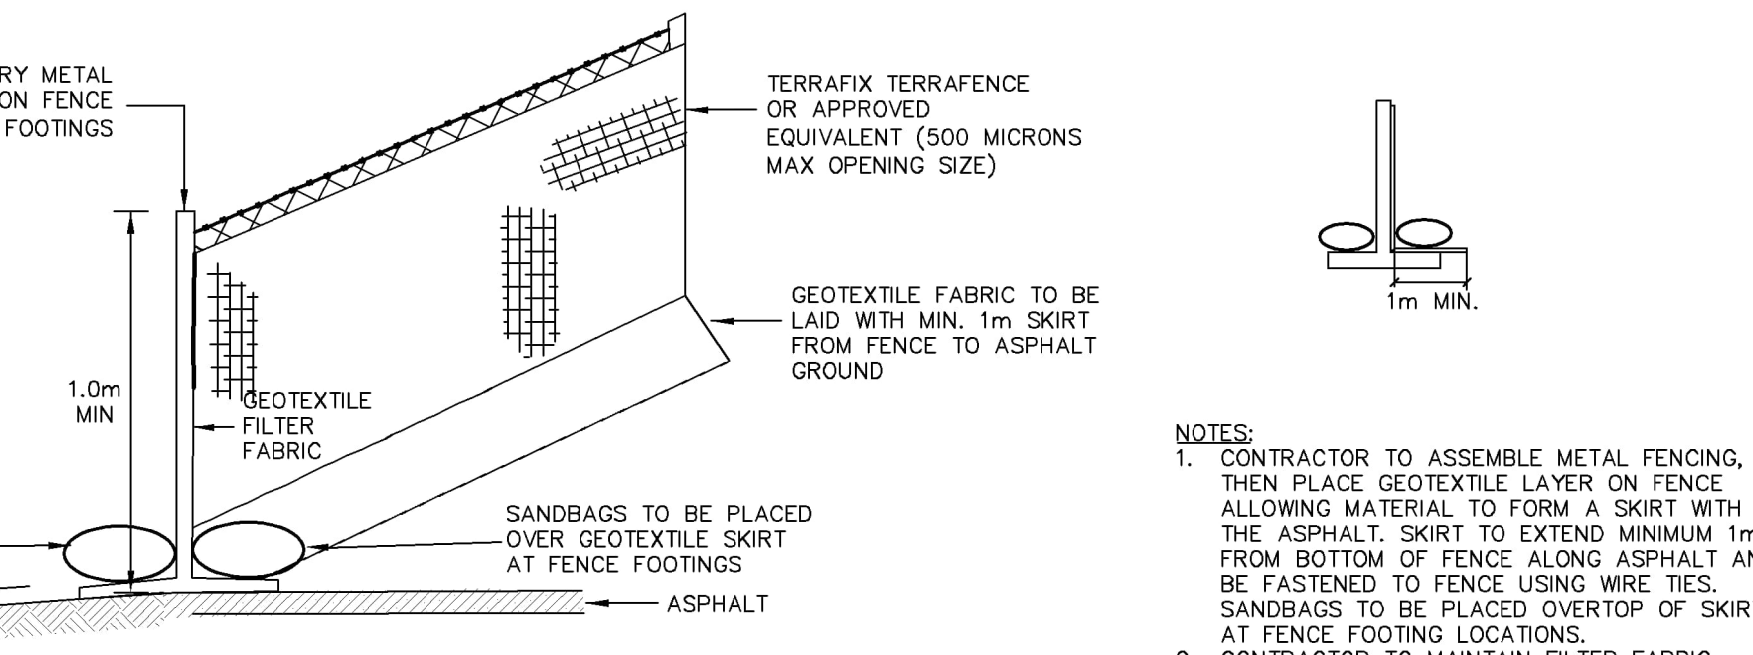


SEDIMENT CONTROL FILTER FABRIC FENCE ON ASPHALT N.T.S.

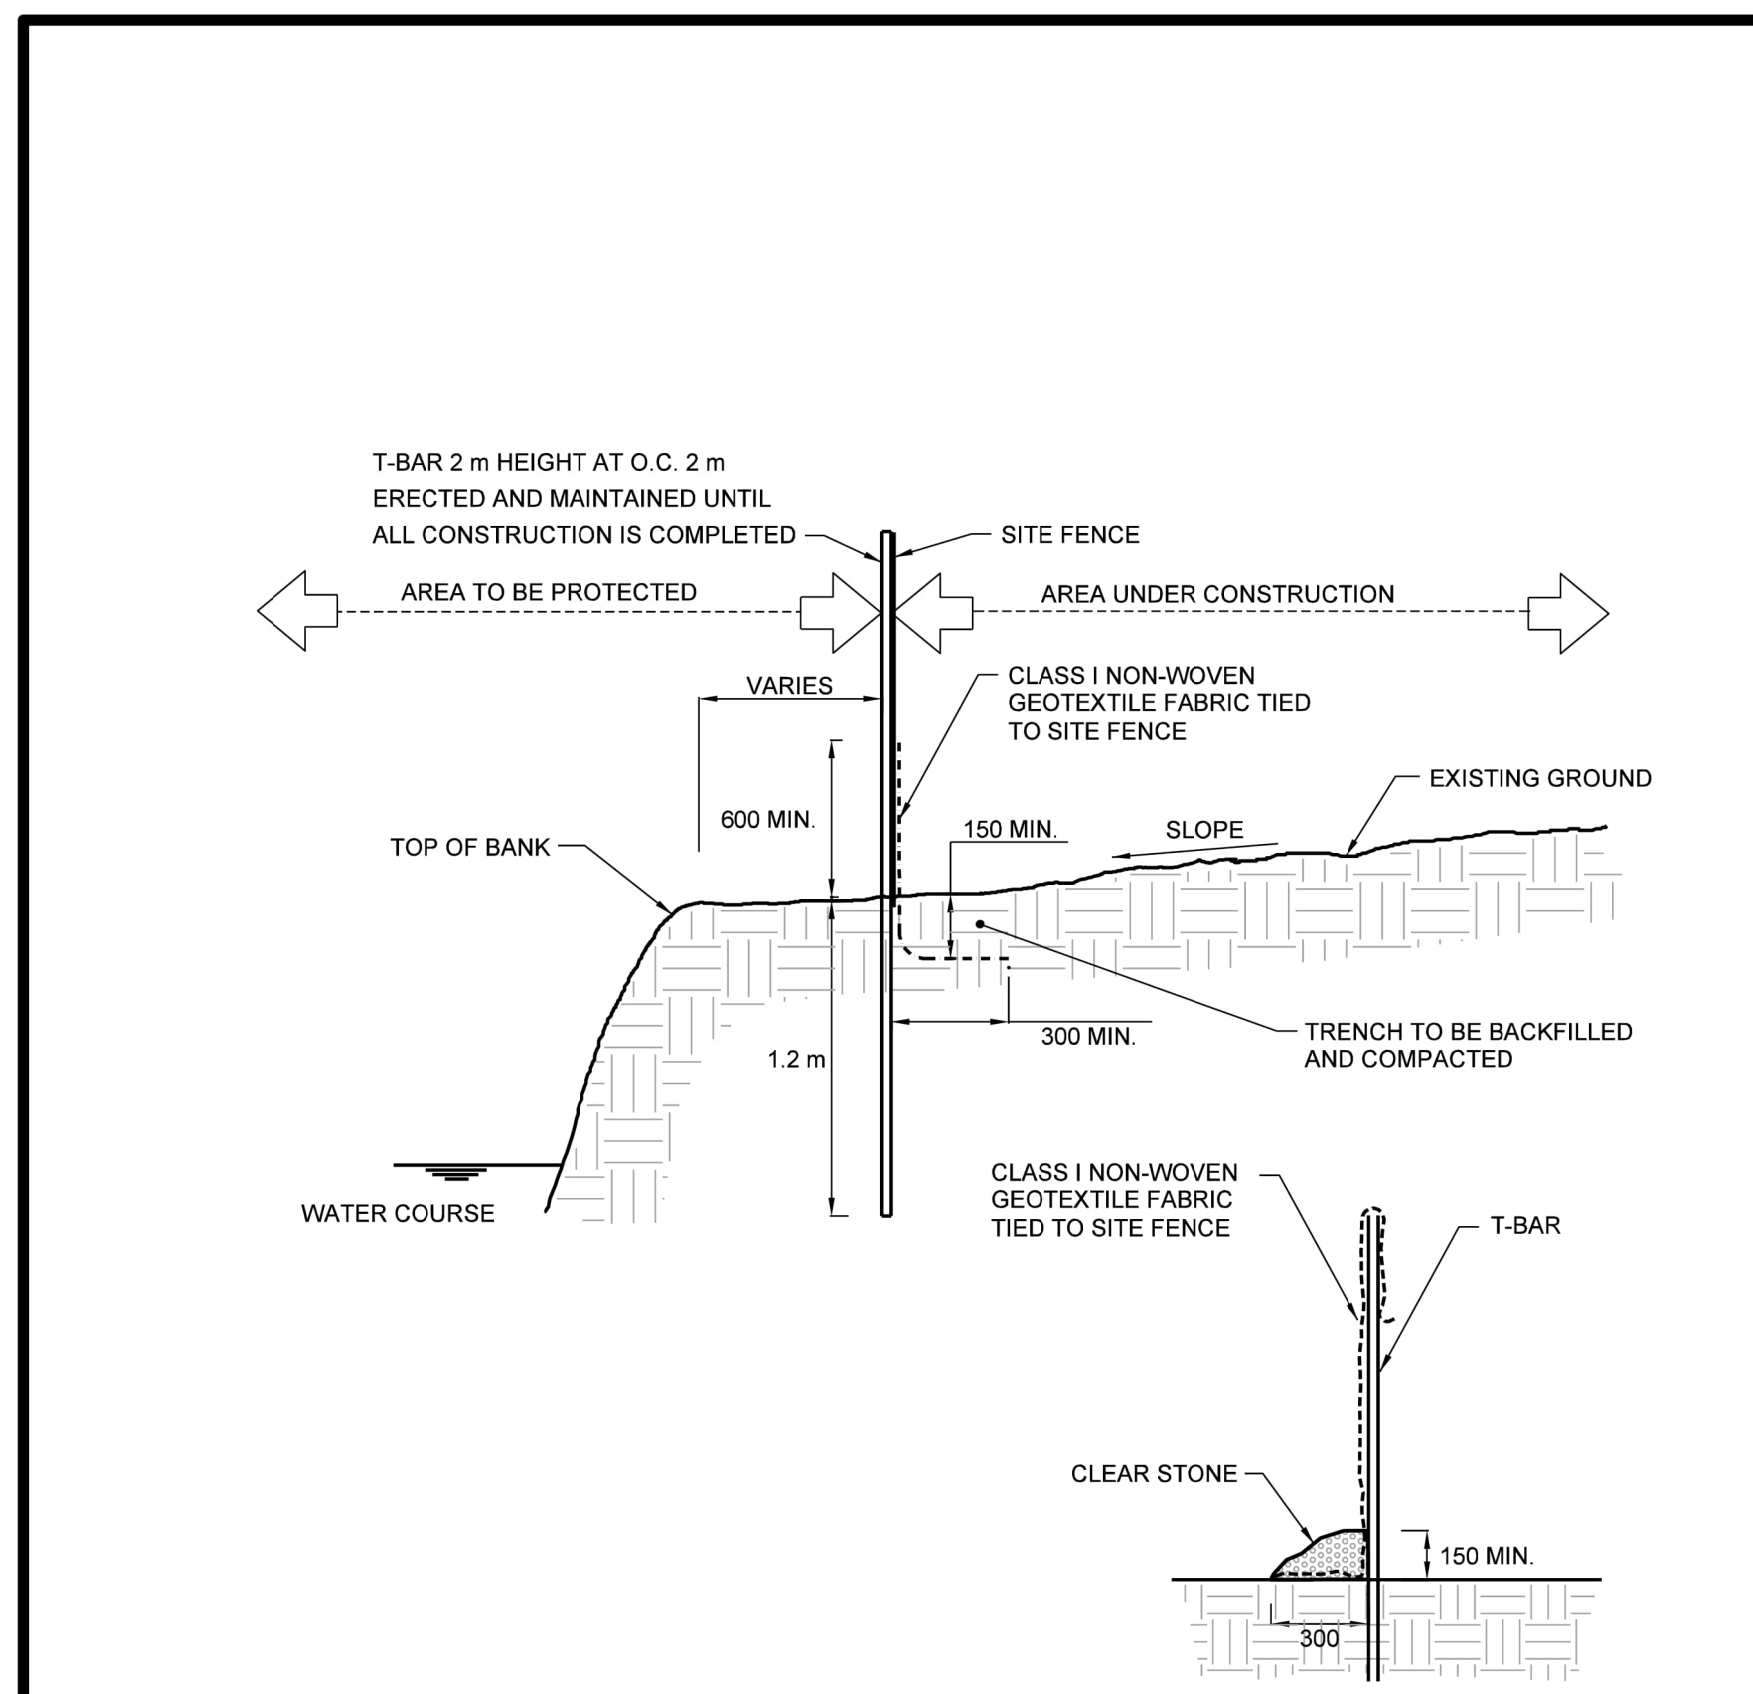

- NOTES:
- MATERIALS REMOVED FROM TRENCH SHALL BE REPLACED ON TOP OF HORIZONTAL PORTION OF FILTER CLOTH.
 - FILTER CLOTH SHALL BE HORIZONTALLY OVERLAPPED 500 mm.
 - SILT FENCE INSTALLATION WORK SHALL AVOID THE DESTRUCTION OF EXISTING WOODY VEGETATION (EG. SHRUBS AND TREES) OTHER THAN THOSE SPECIES WHICH MAY HAVE BEEN APPROVED FOR REMOVAL.

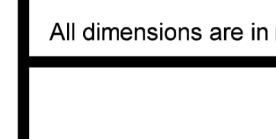

ENGINEERING & CONSTRUCTION SERVICES STANDARD DRAWING
REV 1 NOV 2014
SEDIMENT CONTROL FENCE
T-219.130-1
NTS SHEET 1

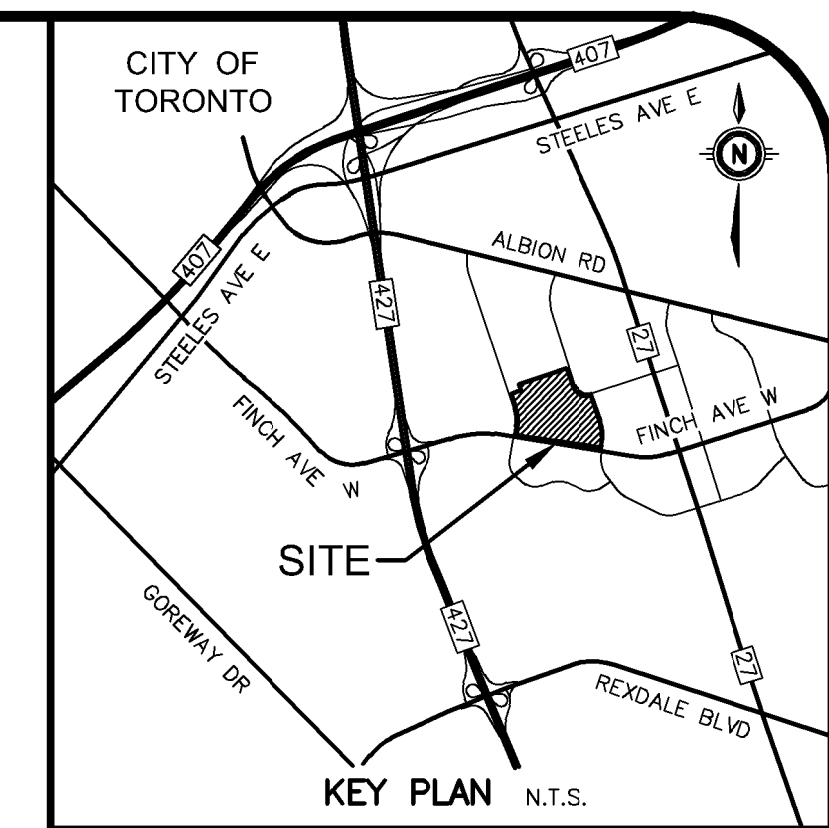

GEODETIC BENCHMARK ELEV. =
BENCHMARK NO. 123187115. SOURCE: COSINE ON-LINE. VERTICAL DATUM: CGVD88/2011. BEARING: 100.00000000. A TABLET IN BRICK WALL ON WEST FACE OF CITY OF TORONTO FIRE STATION #11, ON THE EAST SIDE OF HAMBURLEIGH DR. 0.50M FROM NORTHWEST CORNER OF BUILDING. 0.52M ABOVE PAVEMENT ELEVATION = 170.690 METRES

SITE BENCHMARK ELEV. = 170.690 m
SITE BENCHMARKS ARE SHOWN ON THE FACE OF THIS PLAN.

NOTE TO CONTRACTOR:
DO NOT SCALE DRAWINGS.
CONTRACTORS MUST CHECK AND VERIFY ALL DIMENSIONS AND REPORT ANY DISCREPANCIES TO THE ENGINEER BEFORE PROCEEDING WITH THE WORK.
ALL DRAWINGS REMAIN THE PROPERTY OF THE ENGINEER AND SHALL NOT BE REPRODUCED OR REUSED WITHOUT THE ENGINEER'S WRITTEN PERMISSION.
THE OWNER/ARCHITECT/CONTRACTOR IS ADVISED THAT M.T.E. CONSULTANTS INC. CANNOT CORRECT ANY COMPONENT OF THE SITE WORKS NOT INSPECTED DURING CONSTRUCTION. IT IS THE RESPONSIBILITY OF THE GENERAL CONTRACTOR TO NOTIFY M.T.E. CONSULTANTS INC. PRIOR TO COMMENCEMENT OF CONSTRUCTION TO ARRANGE FOR INSPECTION.

NOTE:
1. PROPERTY LINE IS APPROXIMATE ONLY AND SHOULD NOT BE USED FOR DETERMINING SETBACKS OR LAYOUT.
2. EXISTING TOPOGRAPHICAL INFORMATION PROVIDED BY MTE ONTARIO LAND SURVEYORS LTD., DATED JUNE 03, 2020. BEARINGS ARE UTM GRID, DERIVED FROM GPS OBSERVATIONS USING THE CAN-NET NETWORK AND ARE REFERRED TO MTM ZONE 10, NAD83 (CSRS v7) EPOCH 2010.00. DISTANCES ON THIS PLAN ARE GROUND DISTANCES AND CAN BE CONVERTED TO GRID DISTANCES BY MULTIPLYING BY THE COMBINED SCALE FACTOR OF 0.999990016.
3. THIS PLAN IS PART OF A SET OF PLANS WHICH COMPRISE OF THE FOLLOWING: C2.1 AND C2.2.

0 4 8 12 16 20 24m

8.	
7.	
6.	
5.	
4.	
3.	
2.	
1.	

NO. R E V I S I O N



Engineers, Scientists, Surveyors

905-639-2552

CLIENT

PURULATOR INC

5995 AUBURN ROAD SUITE 100 MISSISSAUGA, ON

PROJECT

PURULATOR ETOBICOKE PARKING EXPANSION

325 HUNTER COLLEGE BOULEVARD TORONTO, ON

DRAWING

SITE GRADING AND EROSION AND SEDIMENT CONTROL PLAN FOR TEMPORARY PARKING LOT

Project Manager S. OH Job No. 63287_001

Design By SSO Checked By JRA

Drawn By SDU Checked By SSO

Surveyed By MTE Drawing No.

Date Aug 06/26

Scale 1:300 Sheet 1 of 1

C1.1

HUMBERLINE DRIVE

P.L.N. 07367-0090 (LT)

PART 2, PLAN 66R-2644

(DEDICATED BY BY-LAW 3236, INSTRUMENT 439284)

TEMPORARY GRAVEL PARKING LOT

MATERIAL	DEPTH (mm)
GRANULAR "A" BASE COURSE (mm)	280
GRANULAR "B" SUBBASE COURSE (mm)	350

FINCH AVENUE WEST

(DEDICATED BY BY-LAW 2059, INSTRUMENT B-289983)

P.L.N. 07367-0084 (LT)

PART 1, PLAN 66R-2644

P.L.N. 07367-0083 (LT)

PART 2, PLAN 66R-4734

DEDICATED BY BY-LAW 2059, INSTRUMENT B-289983

LOT 35

CONCESSION 3

SOUTHWEST CORNER LOT 36, CONCESSION 3 FTH

NOTES TO CONTRACTOR:
PRIOR TO CONSTRUCTION, EXISTING UNDERGROUND UTILITIES TO BE CONFIRMED FOR LOCATION, SIZE AND DEPTHS. INFORMATION TO BE PROVIDED TO THE ENGINEER PRIOR TO CONSTRUCTION.